


लागू गट.नं.५८०

मौजे: पसुरे

तर्फ वेळवंड खोरे तालुका : भोर

जिल्हा : पुणे


उत्तर

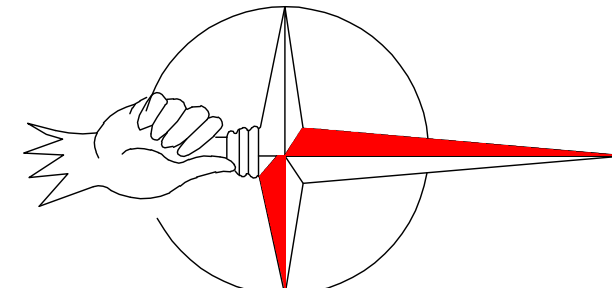

प्रमाण—१ : १०००

गट.नं.५७९ पैकी

लागू गट.नं.५७९ पैकी

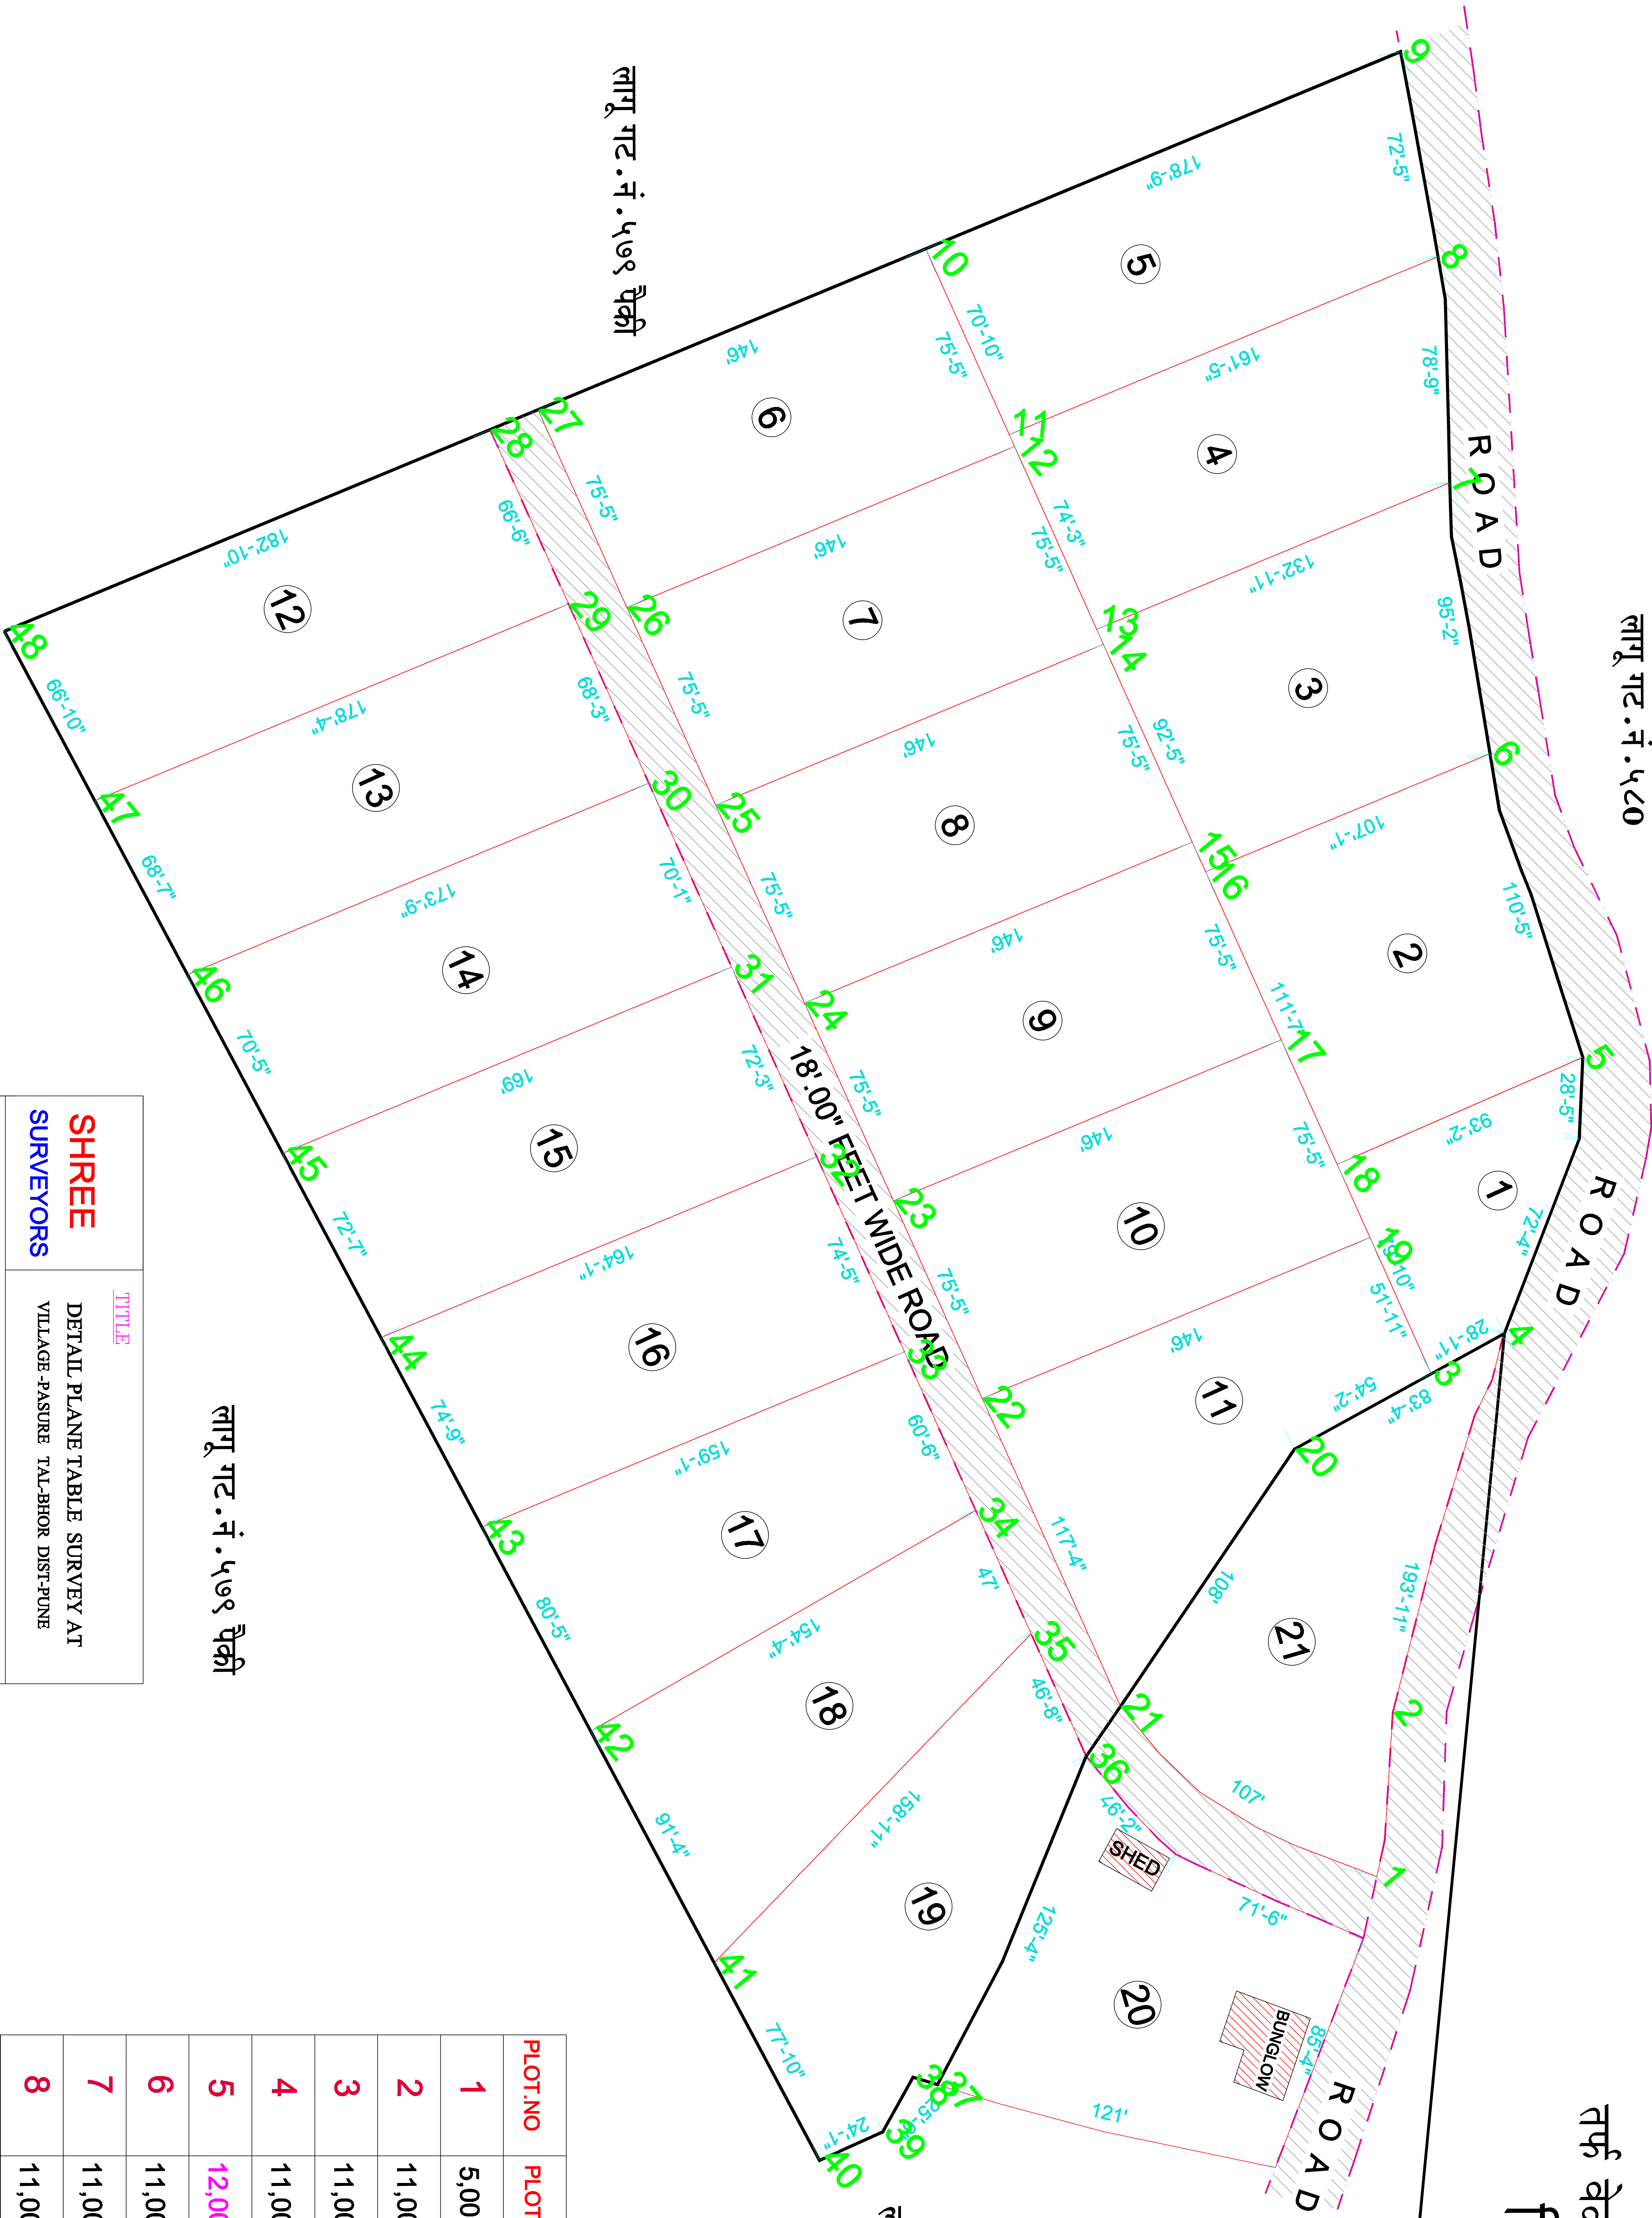

SHREE SURVEYORS	TITLE
	DETAIL PLANE TABLE SURVEY AT VILLAGE-PASURE TAL-BHOR DIST-PUNE

CLINT NAME : Mr- SURYAWANSHI SIR
Mo:- 9823459929

DWG. SCALE 1 : 1000
DATE : 05-09-2025

PH. 9821195171

S No.54/8, Narhe man point,Opp. Navle Bridge,Narhe Gaon,Pune-411041.

Email Id : shreesurveyors51@gmail.com

PLOT.NO	PLOT AREA	PLOT.NO	PLOT AREA
1	5,000.0Sq.ft.	12	12,000.0Sq.ft.
2	11,000.0Sq.ft.	13	12,000.0Sq.ft.
3	11,000.0Sq.ft.	14	12,000.0Sq.ft.
4	11,000.0Sq.ft.	15	12,000.0Sq.ft.
5	12,000.0Sq.ft.	16	12,000.0Sq.ft.
6	11,000.0Sq.ft.	17	11,000.0Sq.ft.
7	11,000.0Sq.ft.	18	10,500.0Sq.ft.
8	11,000.0Sq.ft.	19	10,500.0Sq.ft.
9	11,000.0Sq.ft.	20	11,500.0Sq.ft.
10	11,000.0Sq.ft.	21	11,500.0Sq.ft.
11	11,000.0Sq.ft.		

लागू गट.नं.५७९ पैकी

लागू गट.नं.५७९ पैकी

या प्रमाणे मोजणी प्लॉट ची हद्द असे .

या प्रमाणे गट नं.ची हद्द असे .

या प्रमाणे जागेवर झाडे असे .

